DOVER STATION

ELECTRIC SUBSTATION

TOWN OF DOVER, DUTCHESS COUNTY, NEW YORK

TAX PARCEL 132600-7061-00-698172

Dover Station
A New York Transco Project

APPLICANT

NEW YORK TRANSCO
ONE HUDSON CITY CENTER, STE 300
HUDSON, NY 12534
PHONE: 518-444-4880

ENGINEER/LANDSCAPE ARCHITECT

POWER ENGINEERS, INC.
DBA POWER ENGINEERS CONSULTING, PC
2 HAMPSHIRE ST, STE 301
FOXBOROUGH, MA 02035
PHONE: 774-643-1800

SURVEYOR

BL COMPANIES
355 RESEARCH PARKWAY
MERIDEN, CT 06450
PHONE: 203-630-1406

GEOTECHNICAL ENGINEER

TERRACON CONSULTANTS-NY, INC.
30 CORPORATE CIR STE 201
ALBANY, NY 12203
PHONE: 518-226-0310

ENVIRONMENTAL PERMITTING AND SWPPP

TRC COMPANIES, INC
10 MAXWELL DR STE 200
CLIFTON PARK, NY 12065
PHONE: 518-527-2751

OWNER OF RECORD


MARIO BOCCAROSSA
91 TWIN OAK LANE
WILTON, CT 06897

DRAWING INDEX

CIVIL DRAWINGS	
DWG NO	TITLE
BS-1	EXISTING CONDITIONS MAP
DVB-E1-101	LOCATION MAP
DVB-E1-102	SITE PLAN
DVB-C1-101	GRADING PLAN
DVB-C1-102	DRAINAGE PLAN
DVB-C1-103	TRAFFIC FLOW PLAN
DVB-C1-104	EROSION CONTROL PLAN
DVB-C1-112	SITE DETAILS
DVB-C1-113	SITE DETAILS
DVB-C1-114	SITE DETAILS
DVB-C1-115	SPECIES AVOIDANCE AND CONSERVATION DETAILS
DVB-C1-120	LANDSCAPING PLAN

ELECTRICAL DRAWINGS	
DWG NO	TITLE
DVB-E2-110	NORTH ELEVATION
DVB-E2-111	WEST ELEVATION
DVB-E7-101	LIGHTING PLAN

Dig Safely. New York Call 811 before you dig

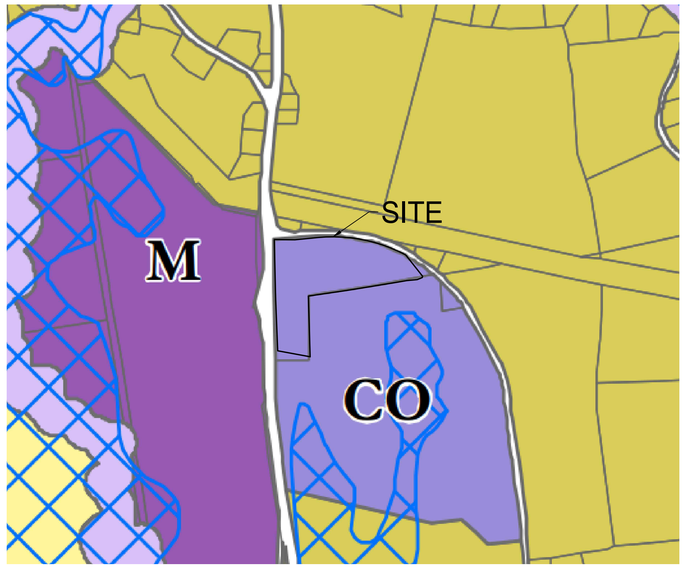

TOWN OF DOVER ZONING MAP

RU, RURAL DISTRICT
CO, COMMERICAL/INDUSTRY/OFFICE
M, INDUSTRIAL/MANUFACTURING
STREAM CORRIDOR BUFFER OVERLAY
FLOOD PLAIN OVERLAY DISTRICT



VICINITY MAP
SCALE: 1" = 2000'

0 1000 2000 4000 6000 FEET
1" = 2000'

STATE OF NEW YORK
WILLIAM H. ROMINES, JR
104002
LICENSED PROFESSIONAL ENGINEER

WILLIAM H. ROMINES, JR PE # 104002

PROJECT LOCATION:
2238 ROUTE 22
DOVER, NY 12594

THIS DRAWING WAS PREPARED BY POWER ENGINEERS, INC. FOR A SPECIFIC PROJECT, TAKING INTO CONSIDERATION THE SPECIFIC AND UNIQUE REQUIREMENTS OF THE PROJECT. REUSE OF THIS DRAWING OR ANY INFORMATION CONTAINED IN THIS DRAWING FOR ANY PURPOSE IS PROHIBITED UNLESS WRITTEN PERMISSION FROM BOTH POWER AND POWER'S CLIENT IS GRANTED.

New York Transco

REV	REVISIONS	DATE	DRN	DSGN	CKD	APPD
C	TOWN OF DOVER PLANNING BOARD SUBMITTAL	08-31-22	BRG	APG	BHR	BHR
B	TOWN OF DOVER PLANNING BOARD SUBMITTAL	04-26-22	BRG	APG	BHR	BHR
A	TOWN OF DOVER PLANNING BOARD SUBMITTAL	09-14-21	BRG	BHR	BHR	BHR

REFERENCE DRAWINGS

DSGN	BHR	06-22-21
DRN	BRG	06-22-21
CKD	BHR	08-12-22
SCALE:	AS NOTED	

FOR 24x36 DWG ONLY

POWER ENGINEERS

NY TRANSCO

DOVER STATION


COVER SHEET AND INDEX DRAWING


JOB NUMBER 169978

REV C

DRAWING NUMBER DVB-E0-101

DVB-E0-101.DWG

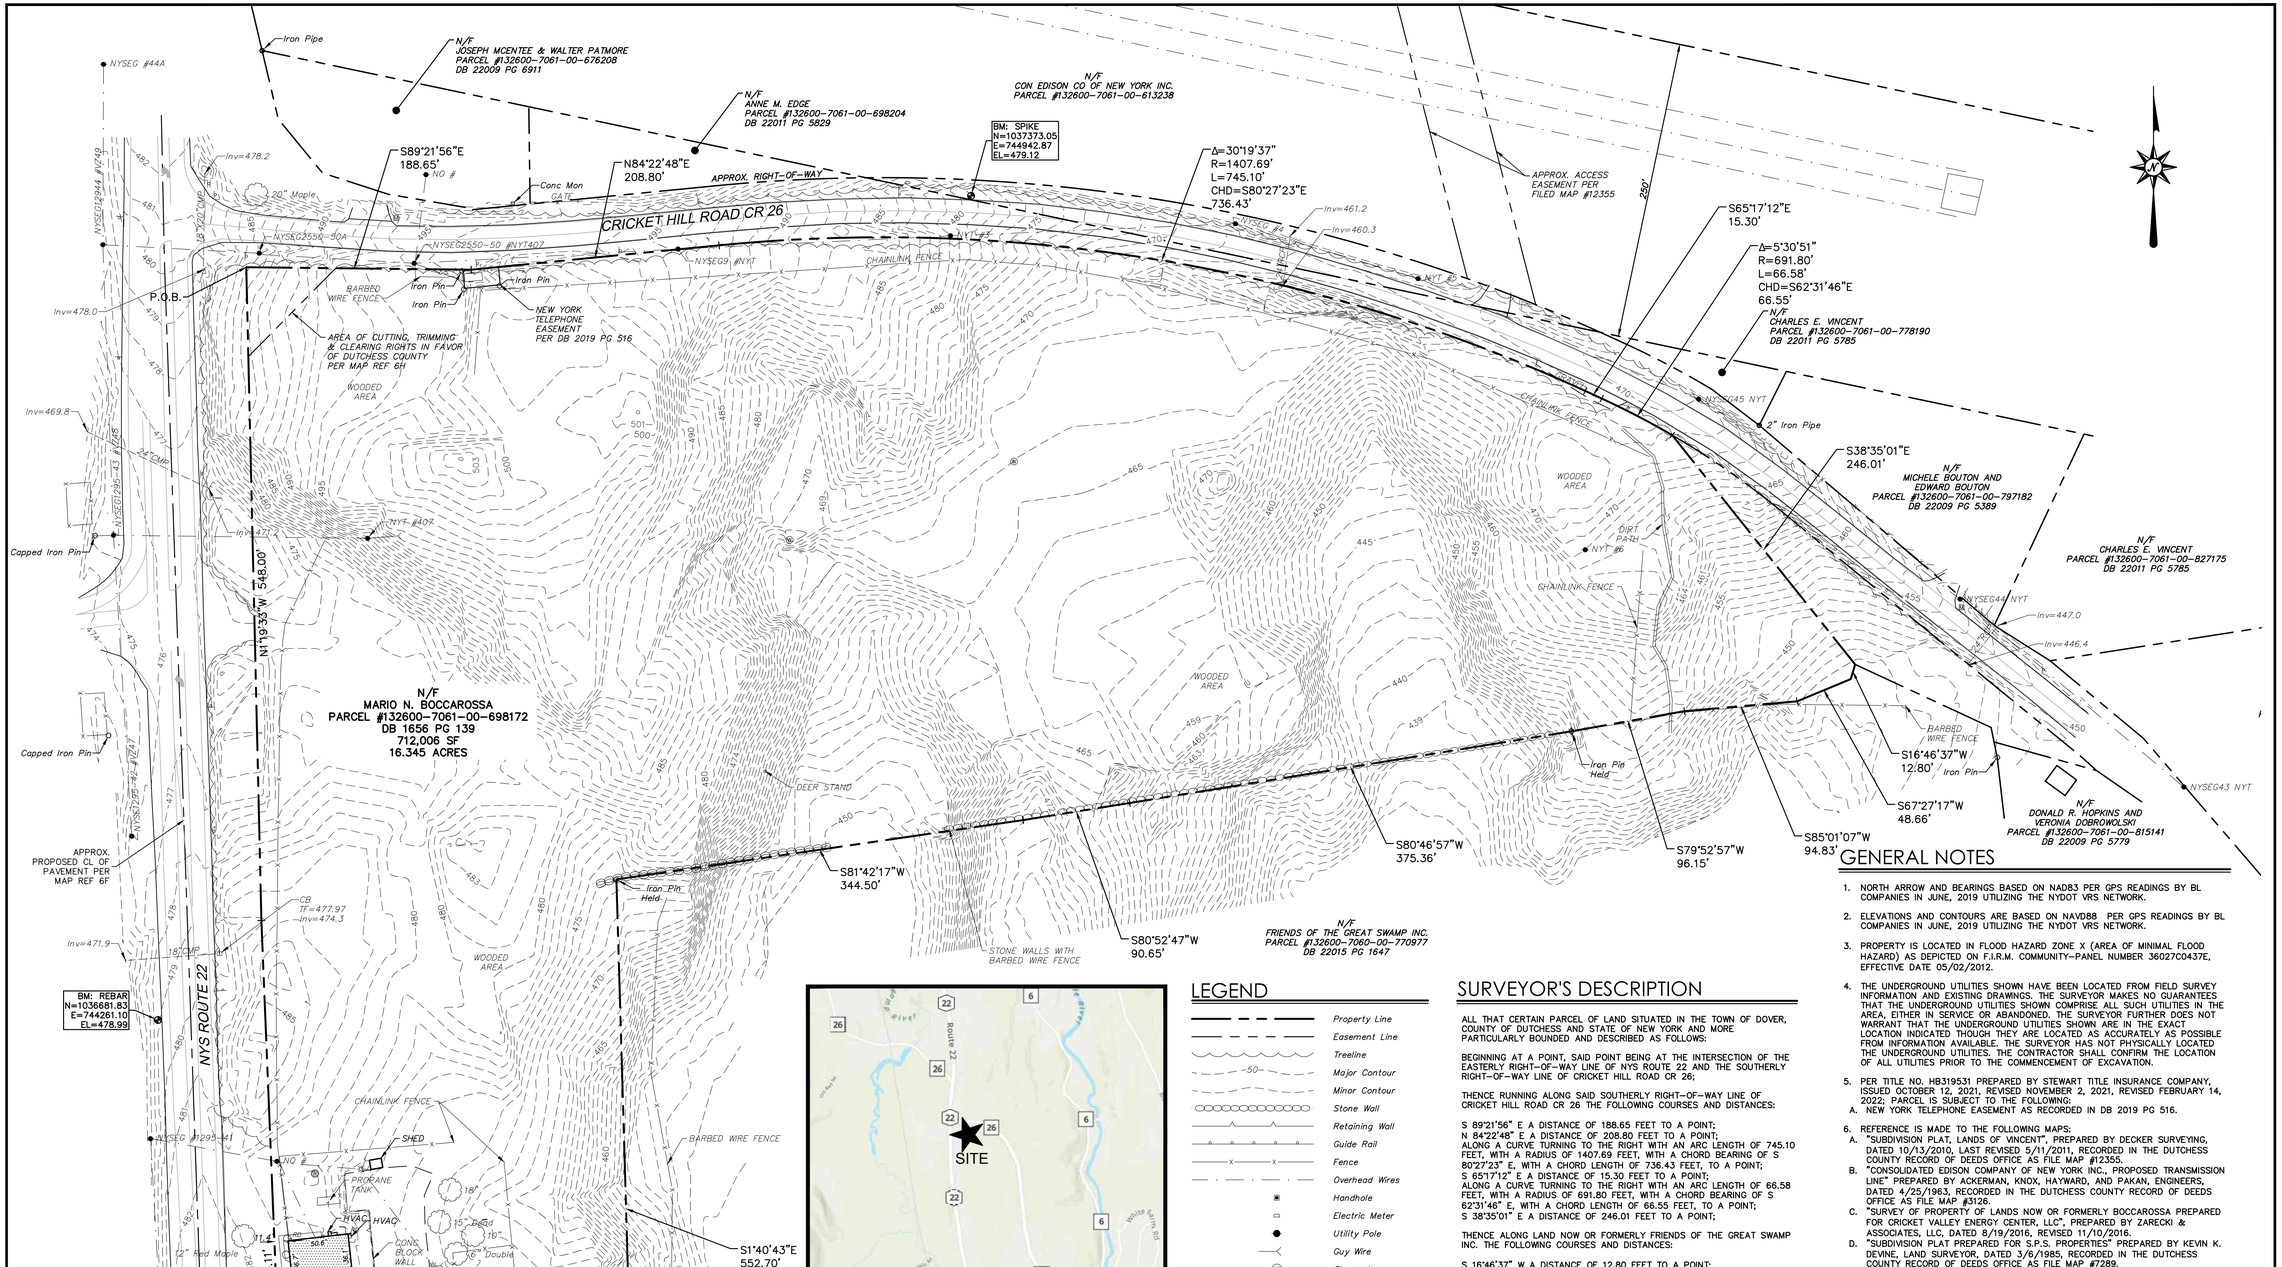

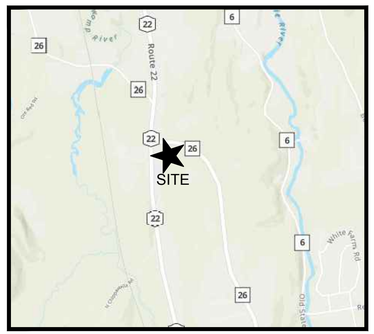

LOCATION MAP

NOT TO SCALE

GRAPHIC SCALE
60 30 0 60
SCALE IN FEET

LEGEND

- Property Line
- Easement Line
- Treeline
- Major Contour
- Minor Contour
- Stone Wall
- Retaining Wall
- Guide Rail
- Fence
- Overhead Wires
- Handhole
- Electric Meter
- Utility Pole
- Guy Wire
- Cleanout
- CB Catch Basin
- MH Manhole
- RD Roof Drain
- Water Well
- Sign
- Mail Box
- Shrub
- Deciduous Tree
- Coniferous Tree

SURVEYOR'S DESCRIPTION

ALL THAT CERTAIN PARCEL OF LAND SITUATED IN THE TOWN OF DOVER, COUNTY OF DUTCHESS AND STATE OF NEW YORK AND MORE PARTICULARLY BOUNDED AND DESCRIBED AS FOLLOWS:

BEGINNING AT A POINT, SAID POINT BEING AT THE INTERSECTION OF THE EASTERLY RIGHT-OF-WAY LINE OF NYS ROUTE 22 AND THE SOUTHERLY RIGHT-OF-WAY LINE OF CRICKET HILL ROAD CR 26;

THENCE RUNNING ALONG SAID SOUTHERLY RIGHT-OF-WAY LINE OF CRICKET HILL ROAD CR 26 THE FOLLOWING COURSES AND DISTANCES:

S 89°21'56" E A DISTANCE OF 188.65 FEET TO A POINT;
N 84°22'48" E A DISTANCE OF 208.80 FEET TO A POINT;
ALONG A CURVE TURNING TO THE RIGHT WITH AN ARC LENGTH OF 745.10 FEET, WITH A RADIUS OF 1407.69 FEET, WITH A CHORD BEARING OF S 80°27'23" E, WITH A CHORD LENGTH OF 736.43 FEET, TO A POINT;
S 65°17'12" E A DISTANCE OF 15.30 FEET TO A POINT;
ALONG A CURVE TURNING TO THE RIGHT WITH AN ARC LENGTH OF 66.58 FEET, WITH A RADIUS OF 691.80 FEET, WITH A CHORD BEARING OF S 62°31'46" E, WITH A CHORD LENGTH OF 66.55 FEET, TO A POINT;
S 38°35'01" E A DISTANCE OF 246.01 FEET TO A POINT;

THENCE ALONG LAND NOW OR FORMERLY FRIENDS OF THE GREAT SWAMP INC. THE FOLLOWING COURSES AND DISTANCES:

S 16°46'37" W A DISTANCE OF 12.80 FEET TO A POINT;
S 67°27'17" W A DISTANCE OF 48.66 FEET TO A POINT;
S 85°01'07" W A DISTANCE OF 94.83 FEET TO A POINT;
S 79°52'57" W A DISTANCE OF 96.15 FEET TO AN IRON PIN HELD;
S 80°46'57" W A DISTANCE OF 375.36 FEET TO A POINT;
S 80°52'47" W A DISTANCE OF 90.65 FEET TO A POINT;
S 81°42'17" W A DISTANCE OF 344.50 FEET TO AN IRON PIN HELD;
S 01°40'43" E A DISTANCE OF 552.70 FEET TO A POINT;
N 79°34'53" W A DISTANCE OF 300.00 FEET TO A POINT;

THENCE ALONG THE EASTERLY RIGHT-OF-WAY LINE OF NYS ROUTE 22 THE FOLLOWING COURSES AND DISTANCES:

N 02°19'33" W A DISTANCE OF 464.11 FEET TO A POINT;
N 01°19'33" W A DISTANCE OF 548.00 FEET TO THE POINT AND PLACE OF BEGINNING.

CONTAINING 712,006 SQUARE FEET OR 16.345 ACRES.

GENERAL NOTES

1. NORTH ARROW AND BEARINGS BASED ON NAD83 PER GPS READINGS BY BL COMPANIES IN JUNE, 2019 UTILIZING THE NYDOT VRS NETWORK.
2. ELEVATIONS AND CONTOURS ARE BASED ON NAVD88 PER GPS READINGS BY BL COMPANIES IN JUNE, 2019 UTILIZING THE NYDOT VRS NETWORK.
3. PROPERTY IS LOCATED IN FLOOD HAZARD ZONE X (AREA OF MINIMAL FLOOD HAZARD) AS DEPICTED ON F.I.R.M. COMMUNITY-PANEL NUMBER 360270C0437E, EFFECTIVE DATE 05/02/2012.
4. THE UNDERGROUND UTILITIES SHOWN HAVE BEEN LOCATED FROM FIELD SURVEY INFORMATION AND EXISTING DRAWINGS. THE SURVEYOR MAKES NO GUARANTEES THAT THE UNDERGROUND UTILITIES SHOWN COMPRISE ALL SUCH UTILITIES IN THE AREA, EITHER IN SERVICE OR ABANDONED. THE SURVEYOR FURTHER DOES NOT WARRANT THAT THE UNDERGROUND UTILITIES SHOWN ARE IN THE EXACT LOCATION INDICATED THOUGH THEY ARE LOCATED AS ACCURATELY AS POSSIBLE FROM INFORMATION AVAILABLE. THE SURVEYOR HAS NOT PHYSICALLY LOCATED THE UNDERGROUND UTILITIES. THE CONTRACTOR SHALL CONFIRM THE LOCATION OF ALL UTILITIES PRIOR TO THE COMMENCEMENT OF EXCAVATION.
5. PER TITLE NO. HB319531 PREPARED BY STEWART TITLE INSURANCE COMPANY, ISSUED OCTOBER 12, 2021, REVISED NOVEMBER 2, 2021, REVISED FEBRUARY 14, 2022; PARCEL IS SUBJECT TO THE FOLLOWING:
   A. NEW YORK TELEPHONE EASEMENT AS RECORDED IN DB 2019 PG 516.
6. REFERENCE IS MADE TO THE FOLLOWING MAPS:
   A. "SUBDIVISION PLAT, LANDS OF VINCENT", PREPARED BY DECKER SURVEYING, DATED 10/13/2010, LAST REVISED 5/11/2011, RECORDED IN THE DUTCHESS COUNTY RECORD OF DEEDS OFFICE AS FILE MAP #12355.
   B. "CONSOLIDATED EDISON COMPANY OF NEW YORK INC., PROPOSED TRANSMISSION LINE" PREPARED BY ACKERMAN, KNOX, HAYWARD, AND PAKAN, ENGINEERS, DATED 4/25/1963, RECORDED IN THE DUTCHESS COUNTY RECORD OF DEEDS OFFICE AS FILE MAP #3126.
   C. "SURVEY OF PROPERTY OF LANDS NOW OR FORMERLY BOCCAROSSA PREPARED FOR CRICKET VALLEY ENERGY CENTER, LLC", PREPARED BY ZARECKI & ASSOCIATES, LLC, DATED 8/19/2016, REVISED 11/10/2016.
   D. "SUBDIVISION PLAT PREPARED FOR S.P.S. PROPERTIES" PREPARED BY KEVIN K. DEVINE, LAND SURVEYOR, DATED 3/6/1985, RECORDED IN THE DUTCHESS COUNTY RECORD OF DEEDS OFFICE AS FILE MAP #7289.
   E. "COUNTY OF DUTCHESS HIGHWAY DEPT., LAND TO BE ACQUIRED", FILE NO. D-20, DATED 8/14/40.
   F. "NEW YORK STATE DEPARTMENT OF PUBLIC WORKS DIVISION OF HIGHWAYS, DIST. NO. 8, WASSAIC-DOVER PLAINS - PAWLING LINE, PT. 1, STATE HIGHWAY NO. 5460" MAP NO. 36-37, DATED 2/10/1937.
   G. "SURVEY MAP SHOWING LANDS OF DOVER AUTO PARTS, INC.", PREPARED BY SPENCER G. ROBINSON, LAST REVISED APRIL 10, 1979.
   H. "MAP OF SURVEY PREPARED FOR BOCCAROSSA" PREPARED BY J. WILLIAM KOMISAR, LLS, DATED JULY 2, 2008.

SURVEY CERTIFICATION

TO: NEW YORK TRANSCO LLC, STEWART TITLE INSURANCE COMPANY, HARRIS BEACH PLLC;

UNAUTHORIZED ALTERATION OR ADDITION TO A SURVEY MAP BEARING A LICENSED LAND SURVEYOR'S SEAL IS A VIOLATION OF SECTION 7209, SUBDIVISION 2, OF THE NEW YORK STATE EDUCATION LAW.

ONLY COPIES FROM THE ORIGINAL OF THIS SURVEY MARKED WITH AN ORIGINAL OF THE LAND SURVEYOR'S EMBOSSED SEAL SHALL BE CONSIDERED TO BE VALID TRUE COPIES.

CERTIFICATIONS INDICATED HEREON SIGNIFY THAT THIS SURVEY WAS PREPARED IN ACCORDANCE WITH THE EXISTING CODE OF PRACTICE FOR LAND SURVEYORS ADOPTED BY THE NEW YORK STATE ASSOCIATION OF PROFESSIONAL LAND SURVEYORS. SAID CERTIFICATIONS SHALL RUN ONLY TO THE PERSON FOR WHOM THE SURVEY IS PREPARED, AND ON HIS BEHALF TO THE TITLE COMPANY, GOVERNMENTAL AGENCY AND LENDING INSTITUTION LISTED HEREON, AND TO THE ASSIGNEES OF THE LENDING INSTITUTION. CERTIFICATIONS ARE NOT TRANSFERABLE TO ADDITIONAL INSTITUTIONS OR SUBSEQUENT OWNERS.

STATE OF NEW YORK
PATRICK J. CORLESS, JR.
051119
LICENSED LAND SURVEYOR

SIGNED: _____ 4/7/2022

PATRICK J. CORLESS, JR.
L.S. # 051118

Architecture
Engineering
Environmental
Land Surveying

BL Companies

355 Research Parkway
Meriden, CT 06450
(203) 630-1406
(203) 630-2615 Fax

DOVER STATION
2238 NYS ROUTE 22
DOVER, DUTCHESS COUNTY, NEW YORK

REVISIONS		
No.	Date	Desc:
1	6/21/2021	Revised Boundary, Added Approx Centerline
2	8/26/2021	Added Utilities
3	9/24/2021	Revised General Notes
4	10/10/2021	Wetlands, Additional Topography
5	11/18/2021	Title Commitment Review
6	3/25/2022	Revised Title Commitment and Certification
7	3/31/2022	Added Surveyor's Description

Surveyed	RL/JC
Drawn	EB
Reviewed	JM
Scale	1"=60'
Project No.	2100767
Date	6/7/2021
Field Book	FB 562 PG 1-8

CAD File:
EX2100767.01

Title

BOUNDARY & TOPOGRAPHIC SURVEY MAP

Sheet No.


BS-1

Xref (s): _XY2100767.01

Apr 07, 2022 - 1:40pm pcorless G:_JOBS2\1\0x\2100767\DWG\EX2100767.01.dwg
Layout: BL-24X36

© 2022 BL COMPANIES, INC. THESE DRAWINGS SHALL NOT BE UTILIZED BY ANY PERSON, FIRM OR CORPORATION WITHOUT THE SPECIFIC WRITTEN PERMISSION OF BL COMPANIES.

PLAN NORTH

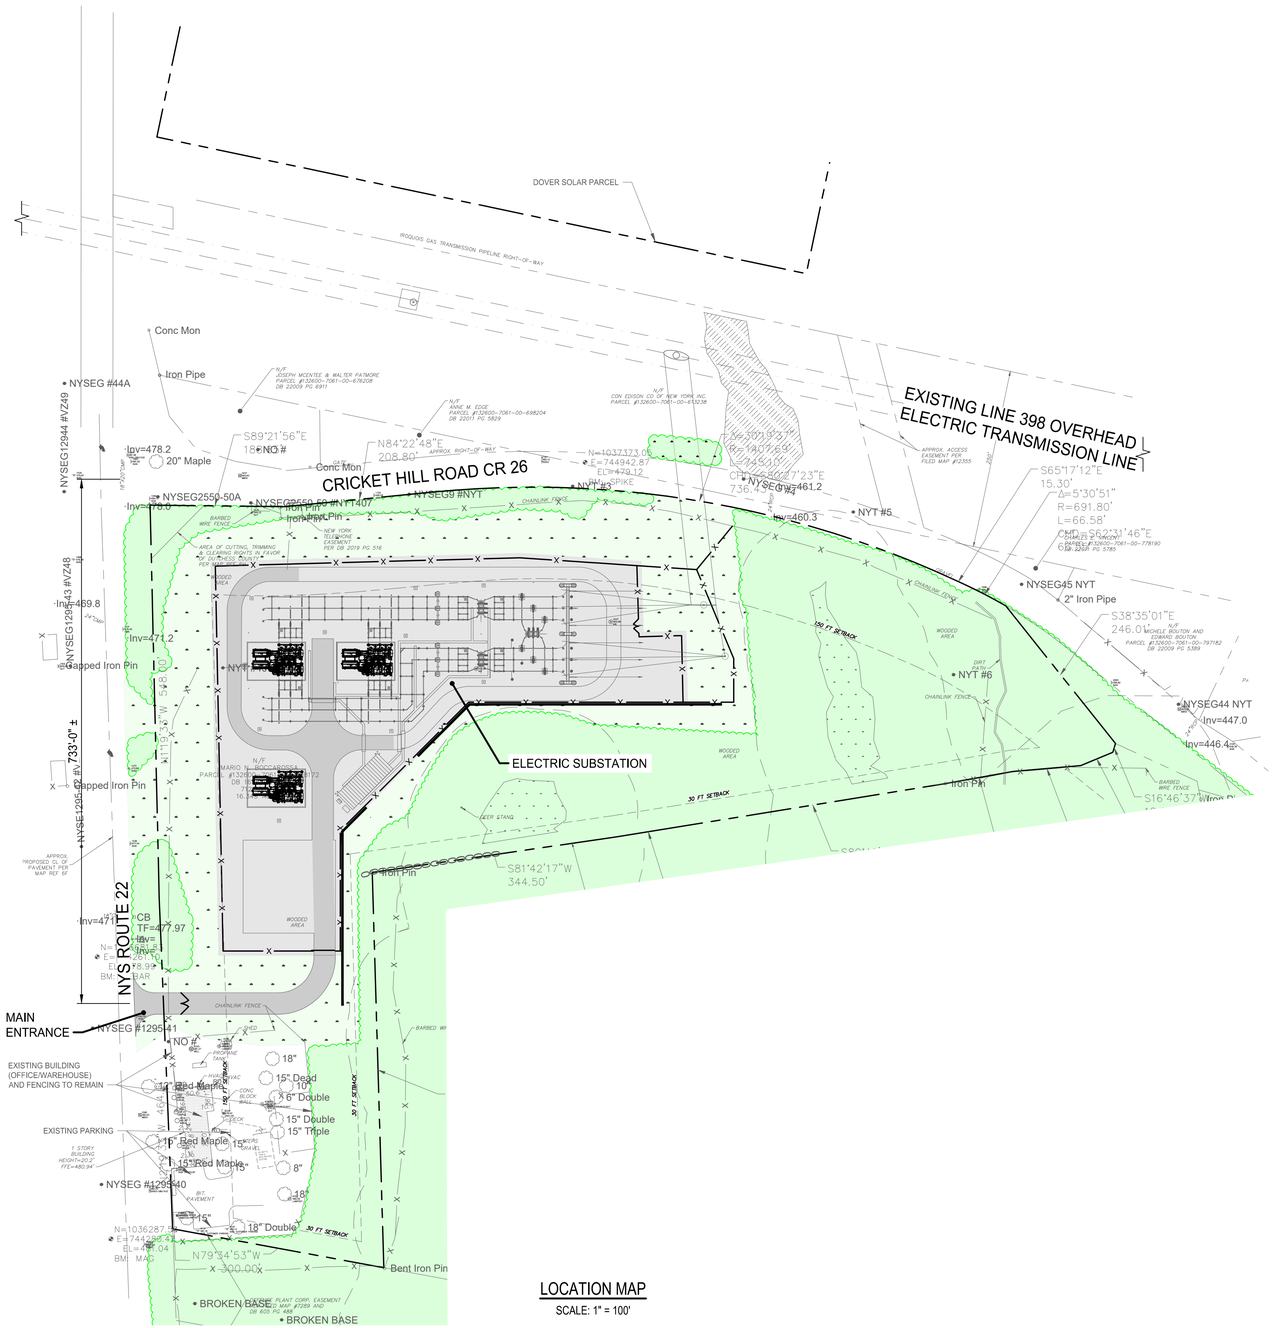

LOCATION MAP
SCALE: 1" = 100'

LEGEND

- PROJECT SITE
- PROPERTY LINE
- PROPOSED FENCE
- PROPOSED PRESERVATION LINE AND PRESERVED WOODED AREA
- PROPOSED LANDSCAPE AND GRASS AREAS
- SUBSTATION AREA SECTION
- ACCESS ROAD SECTION
- EXISTING USACE WETLANDS
- EXISTING NYSDEC WETLANDS
- 100-FT WETLAND BUFFER
- TRANSMISSION POLE
- EXISTING TRANSMISSION POLE
- TRANSMISSION INTERCONNECTION

0 50 100 200 300 FEET
1" = 100'

STATE OF NEW YORK · WILLIAM H. ROMINES, JR · LICENSED PROFESSIONAL ENGINEER · 104002

WILLIAM H. ROMINES, JR PE # 104002

PROJECT LOCATION
2238 ROUTE 22
DOVER, NY 12594

THIS DRAWING WAS PREPARED BY POWER ENGINEERS, INC. FOR A SPECIFIC PROJECT, TAKING INTO CONSIDERATION THE SPECIFIC AND UNIQUE REQUIREMENTS OF THE PROJECT. REUSE OF THIS DRAWING OR ANY INFORMATION CONTAINED IN THIS DRAWING FOR ANY PURPOSE IS PROHIBITED UNLESS WRITTEN PERMISSION FROM BOTH POWER AND POWER'S CLIENT IS GRANTED.

New York Transco

REV	REVISIONS	DATE	DRN	DSGN	CKD	APPD
C	TOWN OF DOVER PLANNING BOARD SUBMITTAL	08-31-22	BRG	APG	BHR	BHR
B	TOWN OF DOVER PLANNING BOARD SUBMITTAL	04-26-22	BRG	APG	BHR	BHR
A	TOWN OF DOVER PLANNING BOARD SUBMITTAL	09-14-21	BRG	BHR	BHR	BHR

REFERENCE DRAWINGS

DSGN	BHR	08-16-21
DRN	BRG	08-16-21
CKD	BHR	08-12-22


SCALE: AS NOTED
FOR 24x36 DWG ONLY

POWER ENGINEERS

NY TRANSCO
DOVER STATION
LOCATION MAP

JOB NUMBER 169978
REV C
DRAWING NUMBER DVB-E1-101

DVB-E1-101.DWG

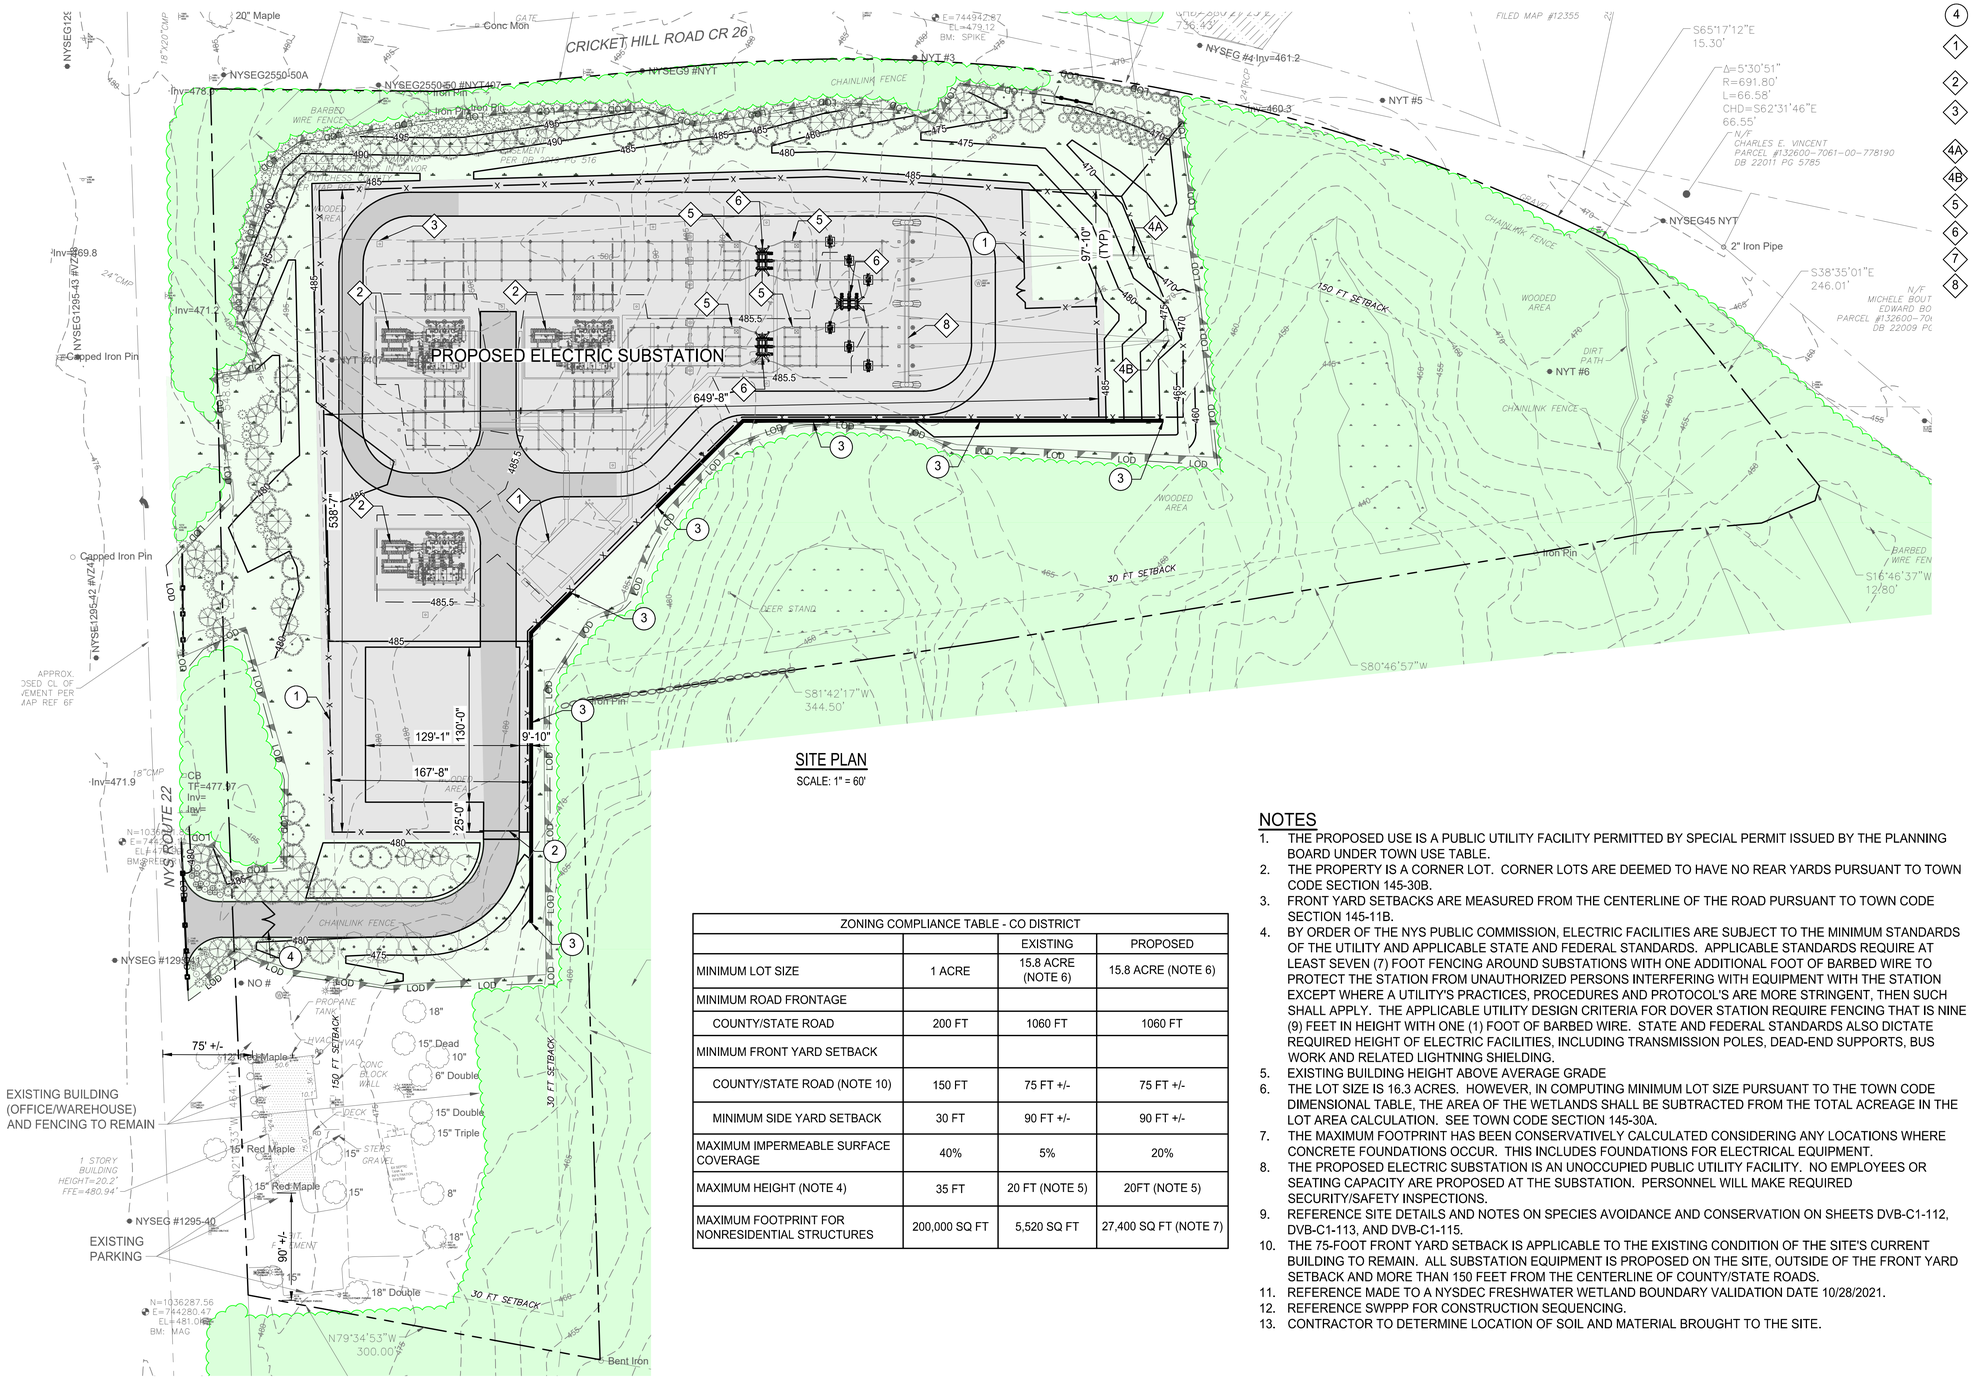

SITE PLAN

SCALE: 1" = 60'

CIVIL KEYNOTES

1. SITE SECURITY CHAIN LINK FENCE (9' MESH, 1' 3 STRAND BARBED WIRE)
2. INSTALL 30' SLIDING GATE
3. RETAINING WALL
4. 34-FT WIDE DOUBLE-LEAF TUBULAR ROW GATE
1. CONTROL UNIT (HEIGHT = 15FT) (DIMENSIONS = 30FT X 80FT)
2. TRANSFORMER (HEIGHT = 33FT)
3. LIGHTNING MAST (TYP) (HEIGHT = 70FT MIN TO 90FT MAX)
4A. 345KV TRANSMISSION LINE POLE (HEIGHT = 145FT)
4B. 345KV TRANSMISSION LINE POLE (HEIGHT = 140FT)
5. 345V DISCONNECT SWITCH
6. 345KV CIRCUIT BREAKER
7. BUS SUPPORT (TYP)
8. DEADEND EQUIPMENT (HEIGHT = 61FT)

LEGEND

- PROJECT SITE
- PROPERTY LINE
- 470 EXISTING CONTOURS
- 470 FINISHED GRADE MAJOR CONTOUR
- 469 FINISHED GRADE MINOR CONTOUR
- 484.5 PROPOSED INTERMEDIATE CONTOURS
- x PROPOSED FENCE
- LOD LIMIT OF DISTURBANCE
- FLOWLINE
- FLOW ARROW
- PROPOSED PRESERVATION LINE AND PRESERVED WOODED AREA
- PROPOSED LANDSCAPE AND GRASS AREAS
- CULVERT
- SUBSTATION AREA SECTION
- ACCESS ROAD SECTION
- RIPRAP
- EXISTING USACE WETLANDS
- EXISTING NYSDEC WETLANDS
- 100-FT WETLAND BUFFER
- TRANSMISSION POLE
- DOUBLE SILT FENCE
- TEMPORARY EXCLUSION GATE

ZONING COMPLIANCE TABLE - CO DISTRICT			
		EXISTING	PROPOSED
MINIMUM LOT SIZE	1 ACRE	15.8 ACRE (NOTE 6)	15.8 ACRE (NOTE 6)
MINIMUM ROAD FRONTAGE			
COUNTY/STATE ROAD	200 FT	1060 FT	1060 FT
MINIMUM FRONT YARD SETBACK			
COUNTY/STATE ROAD (NOTE 10)	150 FT	75 FT +/-	75 FT +/-
MINIMUM SIDE YARD SETBACK	30 FT	90 FT +/-	90 FT +/-
MAXIMUM IMPERMEABLE SURFACE COVERAGE	40%	5%	20%
MAXIMUM HEIGHT (NOTE 4)	35 FT	20 FT (NOTE 5)	20FT (NOTE 5)
MAXIMUM FOOTPRINT FOR NONRESIDENTIAL STRUCTURES	200,000 SQ FT	5,520 SQ FT	27,400 SQ FT (NOTE 7)

NOTES

1. THE PROPOSED USE IS A PUBLIC UTILITY FACILITY PERMITTED BY SPECIAL PERMIT ISSUED BY THE PLANNING BOARD UNDER TOWN USE TABLE.
2. THE PROPERTY IS A CORNER LOT. CORNER LOTS ARE DEEMED TO HAVE NO REAR YARDS PURSUANT TO TOWN CODE SECTION 145-30B.
3. FRONT YARD SETBACKS ARE MEASURED FROM THE CENTERLINE OF THE ROAD PURSUANT TO TOWN CODE SECTION 145-11B.
4. BY ORDER OF THE NYS PUBLIC COMMISSION, ELECTRIC FACILITIES ARE SUBJECT TO THE MINIMUM STANDARDS OF THE UTILITY AND APPLICABLE STATE AND FEDERAL STANDARDS. APPLICABLE STANDARDS REQUIRE AT LEAST SEVEN (7) FOOT FENCING AROUND SUBSTATIONS WITH ONE ADDITIONAL FOOT OF BARBED WIRE TO PROTECT THE STATION FROM UNAUTHORIZED PERSONS INTERFERING WITH EQUIPMENT WITH THE STATION EXCEPT WHERE A UTILITY'S PRACTICES, PROCEDURES AND PROTOCOL'S ARE MORE STRINGENT, THEN SUCH SHALL APPLY. THE APPLICABLE UTILITY DESIGN CRITERIA FOR DOVER STATION REQUIRE FENCING THAT IS NINE (9) FEET IN HEIGHT WITH ONE (1) FOOT OF BARBED WIRE. STATE AND FEDERAL STANDARDS ALSO DICTATE REQUIRED HEIGHT OF ELECTRIC FACILITIES, INCLUDING TRANSMISSION POLES, DEAD-END SUPPORTS, BUS WORK AND RELATED LIGHTNING SHIELDING.
5. EXISTING BUILDING HEIGHT ABOVE AVERAGE GRADE
6. THE LOT SIZE IS 16.3 ACRES. HOWEVER, IN COMPUTING MINIMUM LOT SIZE PURSUANT TO THE TOWN CODE DIMENSIONAL TABLE, THE AREA OF THE WETLANDS SHALL BE SUBTRACTED FROM THE TOTAL ACREAGE IN THE LOT AREA CALCULATION. SEE TOWN CODE SECTION 145-30A.
7. THE MAXIMUM FOOTPRINT HAS BEEN CONSERVATIVELY CALCULATED CONSIDERING ANY LOCATIONS WHERE CONCRETE FOUNDATIONS OCCUR. THIS INCLUDES FOUNDATIONS FOR ELECTRICAL EQUIPMENT.
8. THE PROPOSED ELECTRIC SUBSTATION IS AN UNOCCUPIED PUBLIC UTILITY FACILITY. NO EMPLOYEES OR SEATING CAPACITY ARE PROPOSED AT THE SUBSTATION. PERSONNEL WILL MAKE REQUIRED SECURITY/SAFETY INSPECTIONS.
9. REFERENCE SITE DETAILS AND NOTES ON SPECIES AVOIDANCE AND CONSERVATION ON SHEETS DVB-C1-112, DVB-C1-113, AND DVB-C1-115.
10. THE 75-FOOT FRONT YARD SETBACK IS APPLICABLE TO THE EXISTING CONDITION OF THE SITE'S CURRENT BUILDING TO REMAIN. ALL SUBSTATION EQUIPMENT IS PROPOSED ON THE SITE, OUTSIDE OF THE FRONT YARD SETBACK AND MORE THAN 150 FEET FROM THE CENTERLINE OF COUNTY/STATE ROADS.
11. REFERENCE MADE TO A NYSDEC FRESHWATER WETLAND BOUNDARY VALIDATION DATE 10/28/2021.
12. REFERENCE SWPPP FOR CONSTRUCTION SEQUENCING.
13. CONTRACTOR TO DETERMINE LOCATION OF SOIL AND MATERIAL BROUGHT TO THE SITE.

0 30 60 120 180 FEET

1" = 60'

STATE OF NEW YORK
WILLIAM H. ROMINES, JR
LICENSED PROFESSIONAL ENGINEER
104002

WILLIAM H. ROMINES, JR PE # 104002

PROJECT LOCATION:
2238 ROUTE 22
DOVER, NY 12594

THIS DRAWING WAS PREPARED BY POWER ENGINEERS, INC. FOR A SPECIFIC PROJECT, TAKING INTO CONSIDERATION THE SPECIFIC AND UNIQUE REQUIREMENTS OF THE PROJECT. REUSE OF THIS DRAWING OR ANY INFORMATION CONTAINED IN THIS DRAWING FOR ANY PURPOSE IS PROHIBITED UNLESS WRITTEN PERMISSION FROM BOTH POWER AND POWER'S CLIENT IS GRANTED.

New York Transco

REV	REVISIONS	DATE	DRN	DSGN	CKD	APPD
C	TOWN OF DOVER PLANNING BOARD SUBMITTAL	08-31-22	BRG	APG	BHR	BHR
B	TOWN OF DOVER PLANNING BOARD SUBMITTAL	04-26-22	BRG	APG	BHR	BHR
A	TOWN OF DOVER PLANNING BOARD SUBMITTAL	09-14-21	BRG	BHR	BHR	BHR

REFERENCE DRAWINGS

DSGN	BHR	08-16-21
DRN	BRG	08-16-21
CKD	BHR	08-12-22

SCALE: AS NOTED

FOR 24x36 DWG ONLY

POWER ENGINEERS

NY TRANSCO

DOVER STATION


SITE PLAN

JOB NUMBER 169978

REV C

DRAWING NUMBER DVB-E1-102

DVB-E1-102.DWG

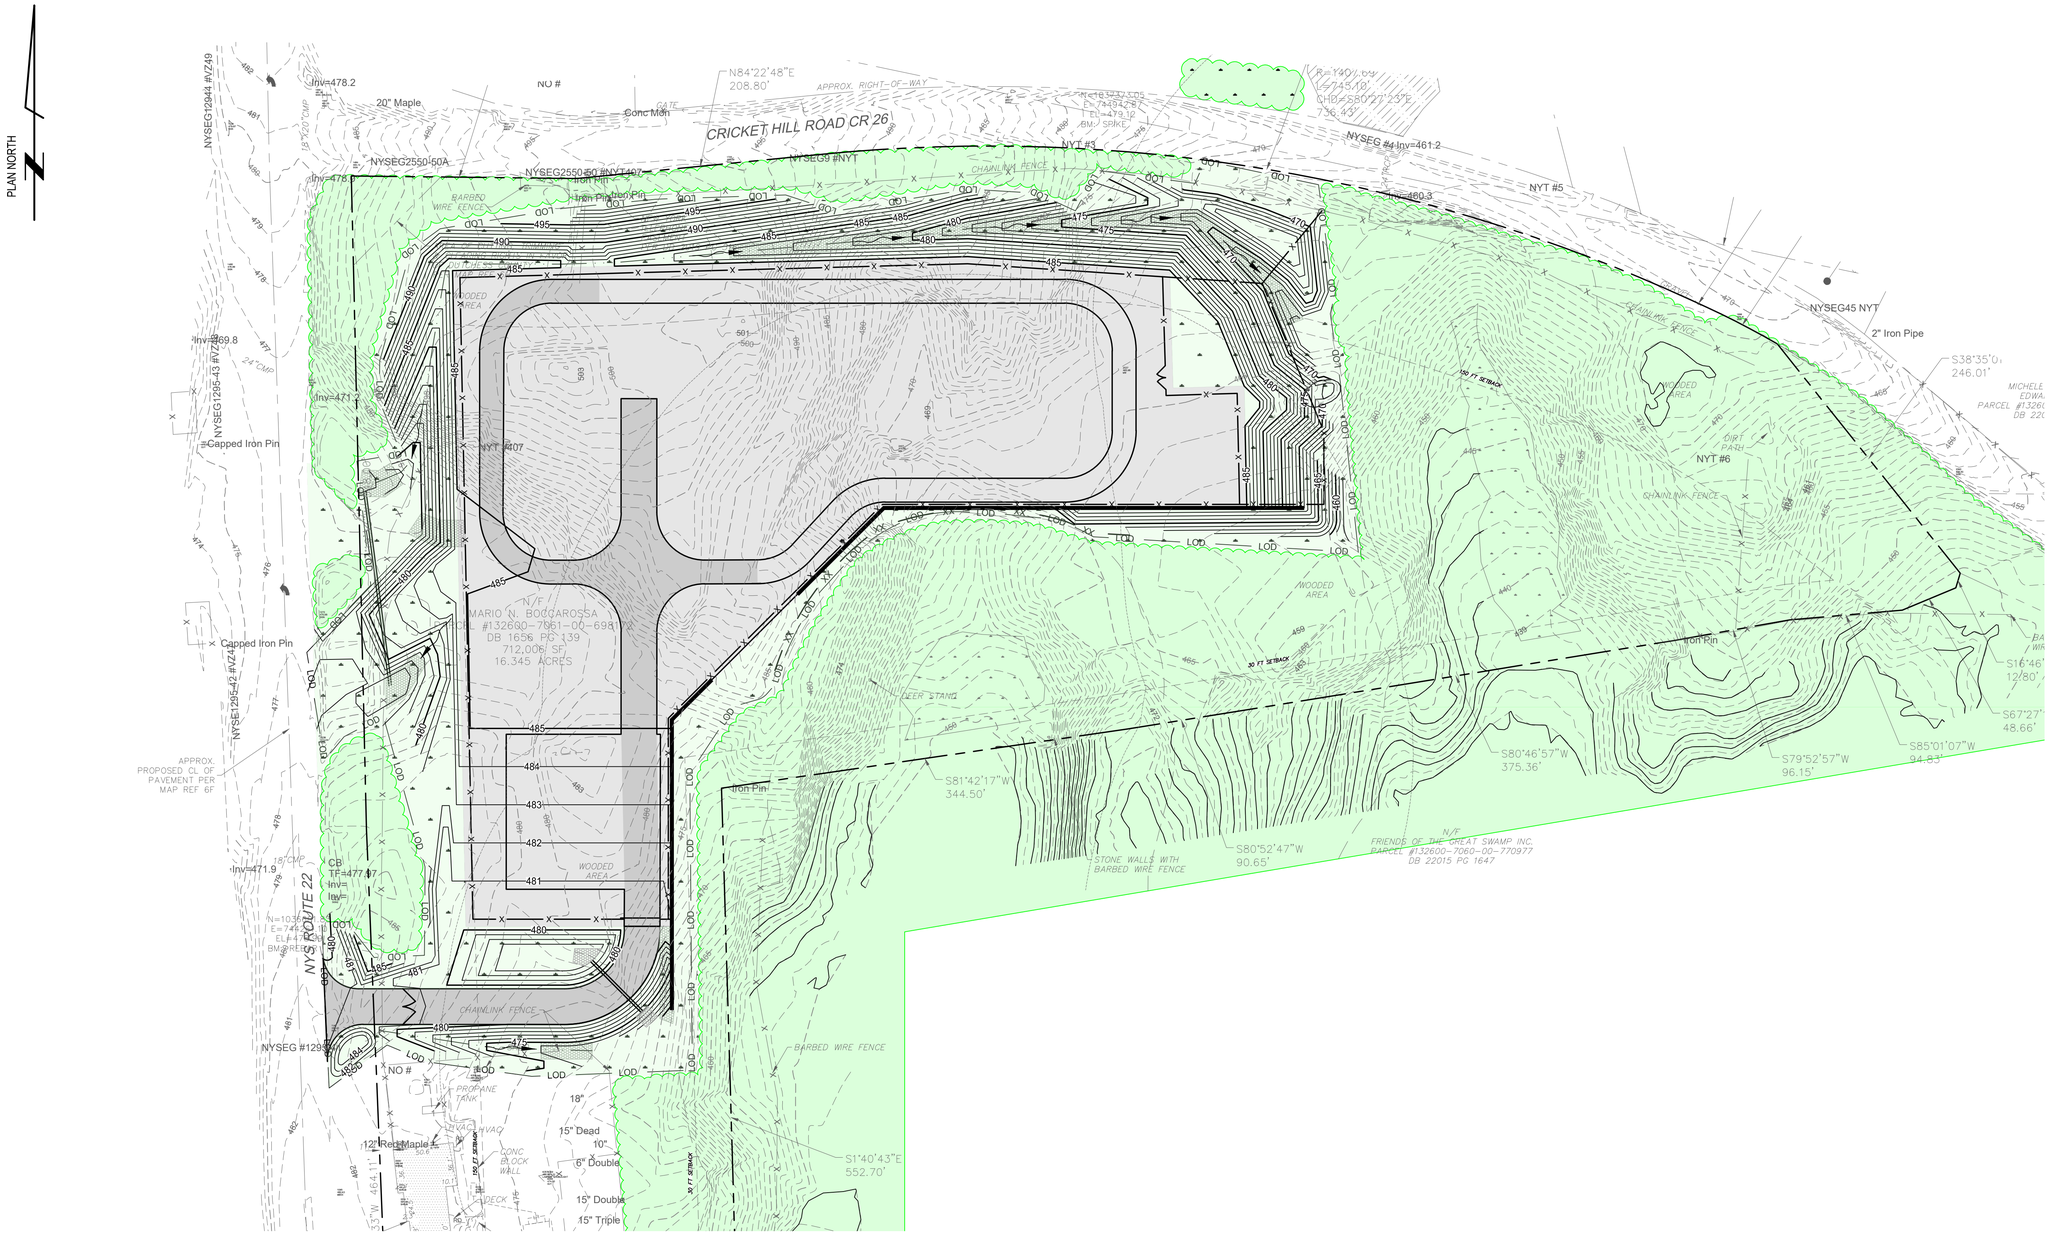

GRADING PLAN

SCALE: 1" = 60'

ESTIMATED QUANTITIES NOTES

1. ALL ESTIMATED MATERIAL QUANTITIES ARE IN-PLACE QUANTITIES AND DO NOT INDICATE ALL MATERIALS REQUIRED TO COMPLETE CONSTRUCTION. ESTIMATED QUANTITIES DO NOT REFLECT CUT OR FILL FACTORS AND DO NOT TAKE OTHER ADJUSTMENTS INTO ACCOUNT. CONTRACTOR SHALL BE RESPONSIBLE FOR VERIFYING ALL QUANTITIES AND MATERIALS AS INDICATED ON THE DRAWINGS.
2. REMOVE MIN 6" OF ORGANIC MATERIAL FROM 7.75 ACRES = 6500 CU YDS
3. STOCKPILE TOPSOIL NEEDED FOR LANDSCAPING AREAS OUTSIDE THE SUBSTATION (6" MIN = 2200 CU YDS) AND HAUL OFF EXCESS.
4. CUT = 10,000 CU YDS (COORDINATE FINAL CUT AMOUNTS WITH BLASTING CONTRACTOR
5. FILL = 28,000 CU YDS
6. COVER ENTIRE SUBSTATION TO 5' OUTSIDE CHAIN LINK FENCE WITH SUBSTATION PAD SECTION:
   - COMPACTED SUBGRADE THEN 10" RESERVOIR COURSE (5,700 CU YDS)
   - THEN 8" TYPE 2 COMPACTED SUBBASE (4,600 CU YDS)
   - THEN 6" SURFACE COURSE MATERIAL (3,450 CU YDS)
7. COVER ACCESS ROAD WITH ACCESS ROAD SECTION:
   - COMPACTED SUBGRADE THEN 6" COMPACTED SUBBASE (650 CU YDS)
   - THEN 4" ASPHALT BINDER COURSE (450 CU YDS)
   - THEN 2" ASPHALT TOP COURSE (225 CU YARDS)

LEGEND

- PROJECT SITE
- PROPERTY LINE
- 470 EXISTING CONTOURS
- 470 FINISHED GRADE MAJOR CONTOUR
- 469 FINISHED GRADE MINOR CONTOUR
- 484.5 PROPOSED INTERMEDIATE CONTOURS
- x PROPOSED FENCE
- XX XX PRESERVATION FENCE
- LOD LIMIT OF DISTURBANCE
- FLOWLINE
- FLOW ARROW
- PROPOSED PRESERVATION LINE AND PRESERVED WOODED AREA
- PROPOSED LANDSCAPE AND GRASS AREAS
- CULVERT
- SUBSTATION AREA SECTION
- ACCESS ROAD SECTION
- RIPRAP
- EXISTING USACE WETLANDS
- EXISTING NYSDEC WETLANDS
- 100-FT WETLAND BUFFER
- TRANSMISSION POLE
- CONSERVATION ZONE 2

0 30 60 120 180 FEET

1" = 60'

STATE OF NEW YORK · WILLIAM H. ROMINES, JR · LICENSED PROFESSIONAL ENGINEER · 104002

WILLIAM H. ROMINES, JR PE # 104002

PROJECT LOCATION:
2238 ROUTE 22
DOVER, NY 12594

DVB-C1-101.DWG

THIS DRAWING WAS PREPARED BY POWER ENGINEERS, INC. FOR A SPECIFIC PROJECT, TAKING INTO CONSIDERATION THE SPECIFIC AND UNIQUE REQUIREMENTS OF THE PROJECT. REUSE OF THIS DRAWING OR ANY INFORMATION CONTAINED IN THIS DRAWING FOR ANY PURPOSE IS PROHIBITED UNLESS WRITTEN PERMISSION FROM BOTH POWER AND POWER'S CLIENT IS GRANTED.


New York Transco

REV	REVISIONS	DATE	DRN	DSGN	CKD	APPD	REFERENCE DRAWINGS
C	TOWN OF DOVER PLANNING BOARD SUBMITTAL	08-31-22	BRG	APG	BHR	BHR	
B	TOWN OF DOVER PLANNING BOARD SUBMITTAL	04-26-22	BRG	APG	BHR	BHR	
A	TOWN OF DOVER PLANNING BOARD SUBMITTAL	09-14-21	BRG	BHR	BHR	BHR	

DSGN	BHR	08-16-21
DRN	BRG	08-16-21
CKD	BHR	08-12-22
SCALE:	AS NOTED	
FOR 24x36 DWG ONLY		

POWER ENGINEERS

NY TRANSCO	JOB NUMBER 169978 · REV C
DOVER STATION	DRAWING NUMBER DVB-C1-101
GRADING PLAN	

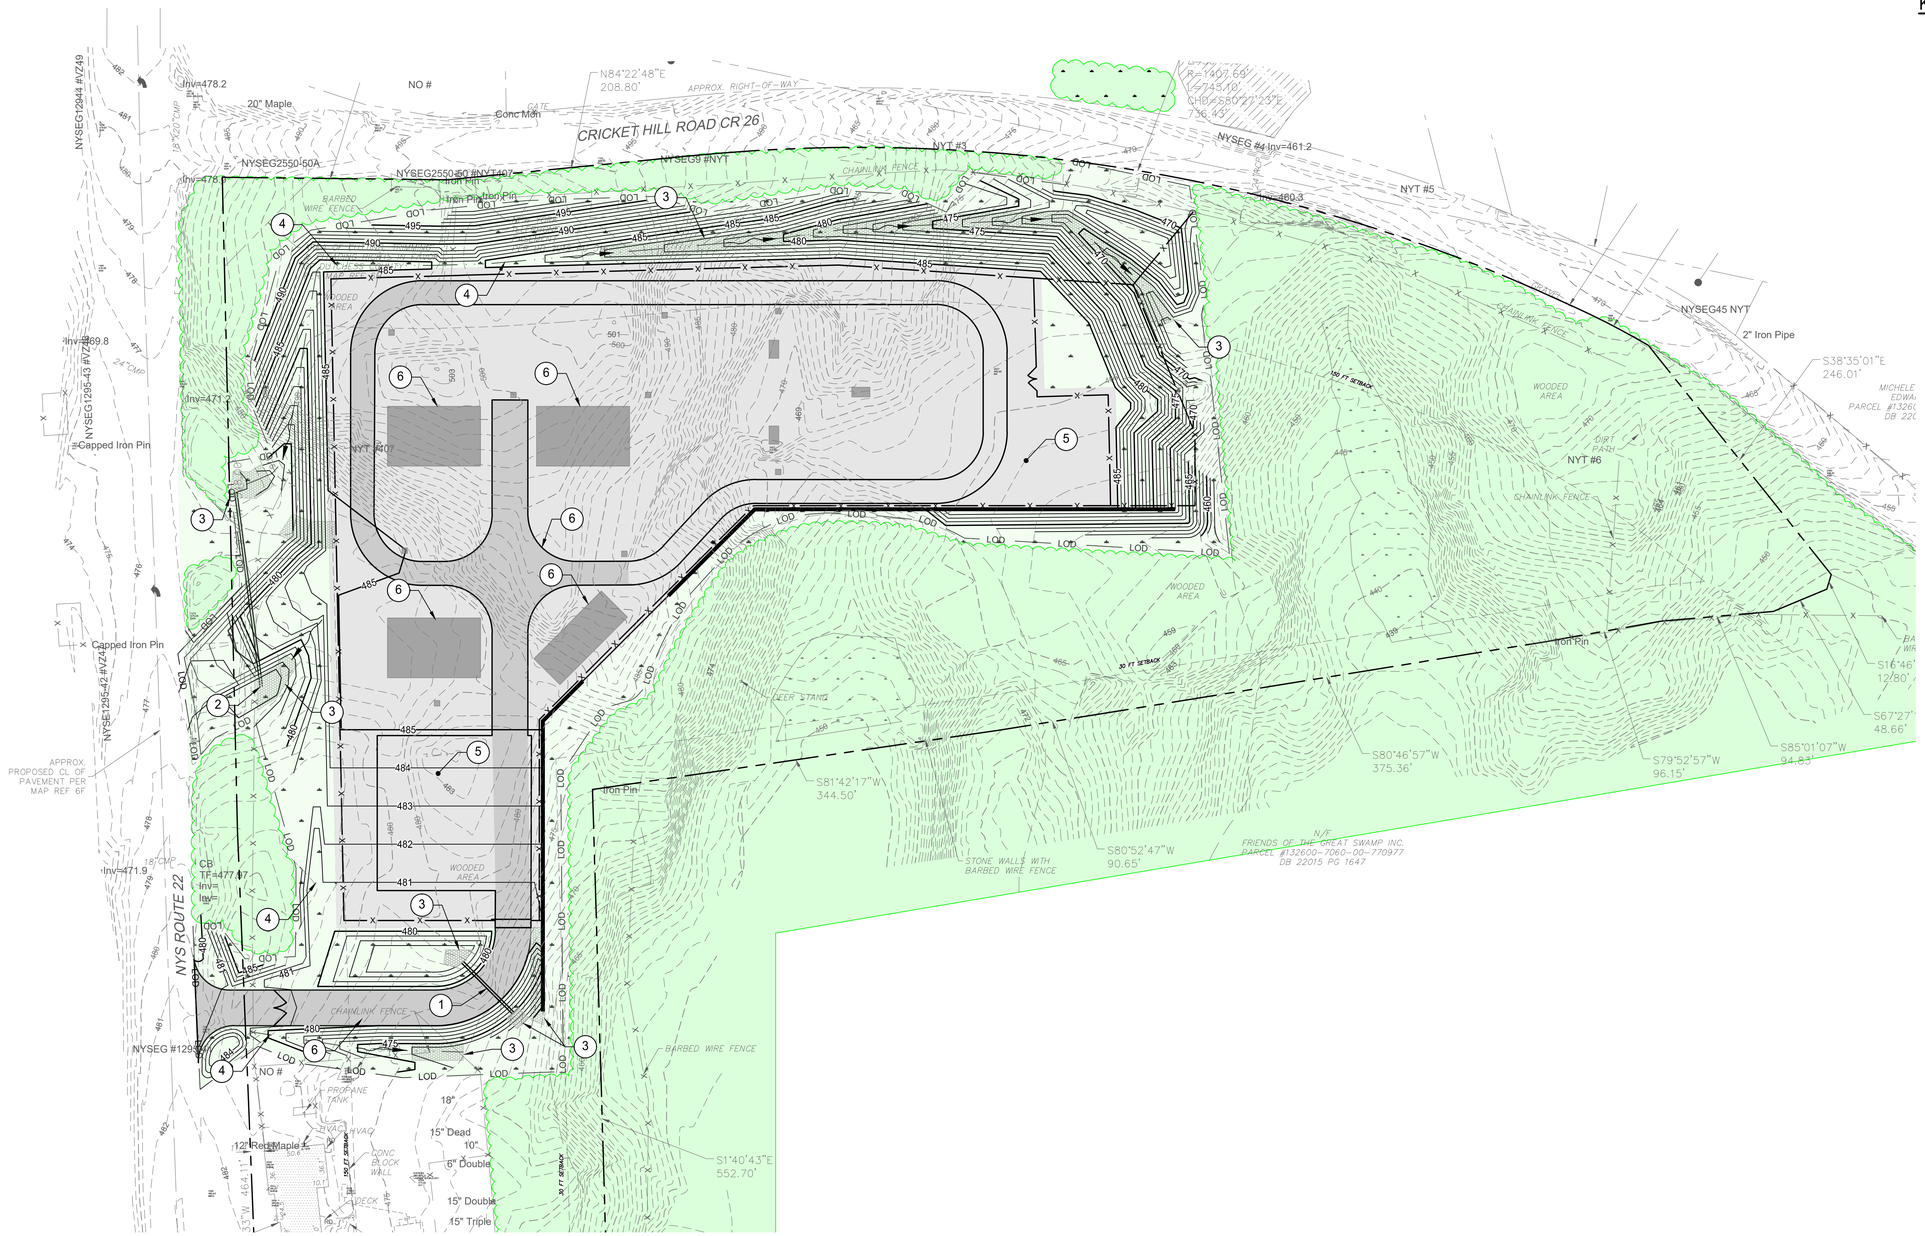

KEYNOTES

1. INSTALL 24" CLASS III RCP PIPE
2. INSTALL 24" CLASS III RCP PIPE
3. INSTALL RIPRAP
4. INSTALL VEGETATED SWALE
5. PERMEABLE SURFACE (SUBSTATION AREA SECTION - SEE DETAIL ON DVB-C1-112)
6. IMPERMEABLE SURFACE (FOUNDATIONS, CONTROL UNIT, ACCESS ROAD SECTION - SEE DETAIL ON DVB-C1-112)

LEGEND

- PROJECT SITE
- PROPERTY LINE
- 470 EXISTING CONTOURS
- 470 FINISHED GRADE MAJOR CONTOUR
- 469 FINISHED GRADE MINOR CONTOUR
- 484.5 PROPOSED INTERMEDIATE CONTOURS
- PROPOSED FENCE
- LOD LIMIT OF DISTURBANCE
- FLOWLINE
- FLOW ARROW
- PROPOSED PRESERVATION LINE AND PRESERVED WOODED AREA
- PROPOSED LANDSCAPE AND GRASS AREAS
- CULVERT
- SUBSTATION AREA SECTION
- ACCESS ROAD SECTION
- RIPRAP
- EXISTING USACE WETLANDS
- EXISTING NYSDEC WETLANDS
- 100-FT WETLAND BUFFER
- TRANSMISSION POLE
- CONSERVATION ZONE 2
- IMPERMEABLE SURFACES WITHIN SUBSTATION

0 30 60 120 180 FEET

1" = 60'

DRAINAGE PLAN

SCALE: 1" = 60'

STATE OF NEW YORK
WILLIAM H. ROMINES, JR
104002
LICENSED PROFESSIONAL ENGINEER

WILLIAM H. ROMINES, JR PE # 104002

PROJECT LOCATION:
2238 ROUTE 22
DOVER, NY 12594

DVB-C1-102.DWG

THIS DRAWING WAS PREPARED BY POWER ENGINEERS, INC. FOR A SPECIFIC PROJECT, TAKING INTO CONSIDERATION THE SPECIFIC AND UNIQUE REQUIREMENTS OF THE PROJECT. REUSE OF THIS DRAWING OR ANY INFORMATION CONTAINED IN THIS DRAWING FOR ANY PURPOSE IS PROHIBITED UNLESS WRITTEN PERMISSION FROM BOTH POWER AND POWER'S CLIENT IS GRANTED.

New York Transco


REV	REVISIONS	DATE	DRN	DSGN	CKD	APPD	REFERENCE DRAWINGS
C	TOWN OF DOVER PLANNING BOARD SUBMITTAL	08-31-22	BRG	APG	BHR	BHR	
B	TOWN OF DOVER PLANNING BOARD SUBMITTAL	04-26-22	BRG	APG	BHR	BHR	
A	TOWN OF DOVER PLANNING BOARD SUBMITTAL	09-14-21	BRG	BHR	BHR	BHR	

DSGN	BHR	08-03-21	
DRN	BRG	08-03-21	
CKD	BHR	08-12-22	
SCALE:	AS NOTED		

FOR 24x36 DWG ONLY

POWER ENGINEERS

NY TRANSCO	JOB NUMBER 169978	REV C
DOVER STATION	DRAWING NUMBER DVB-C1-102	
DRAINAGE PLAN		

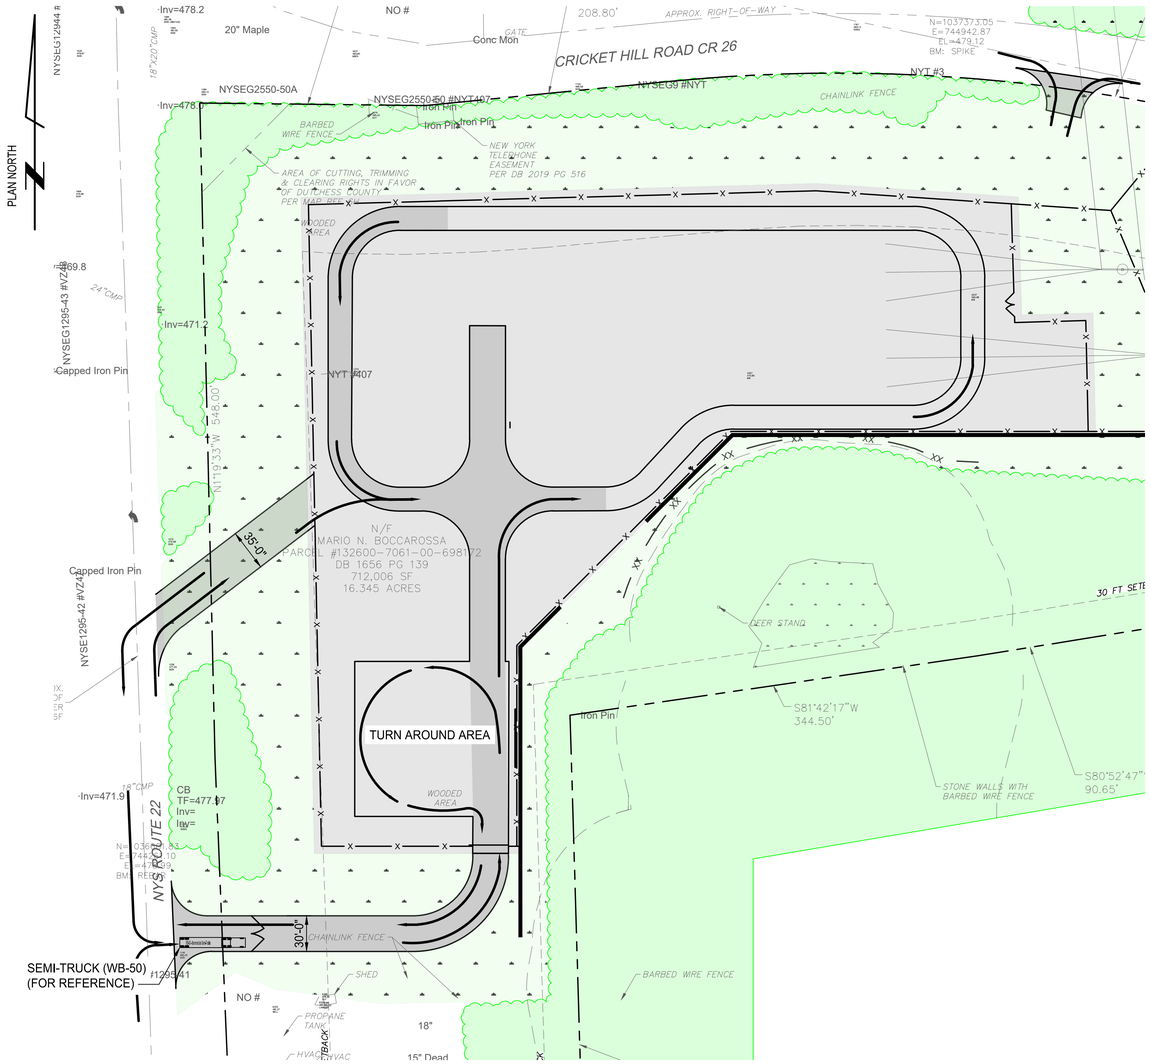


CONSTRUCTION

SCALE: 1" = 60'

0 30 60 120 180 FEET

1" = 60'

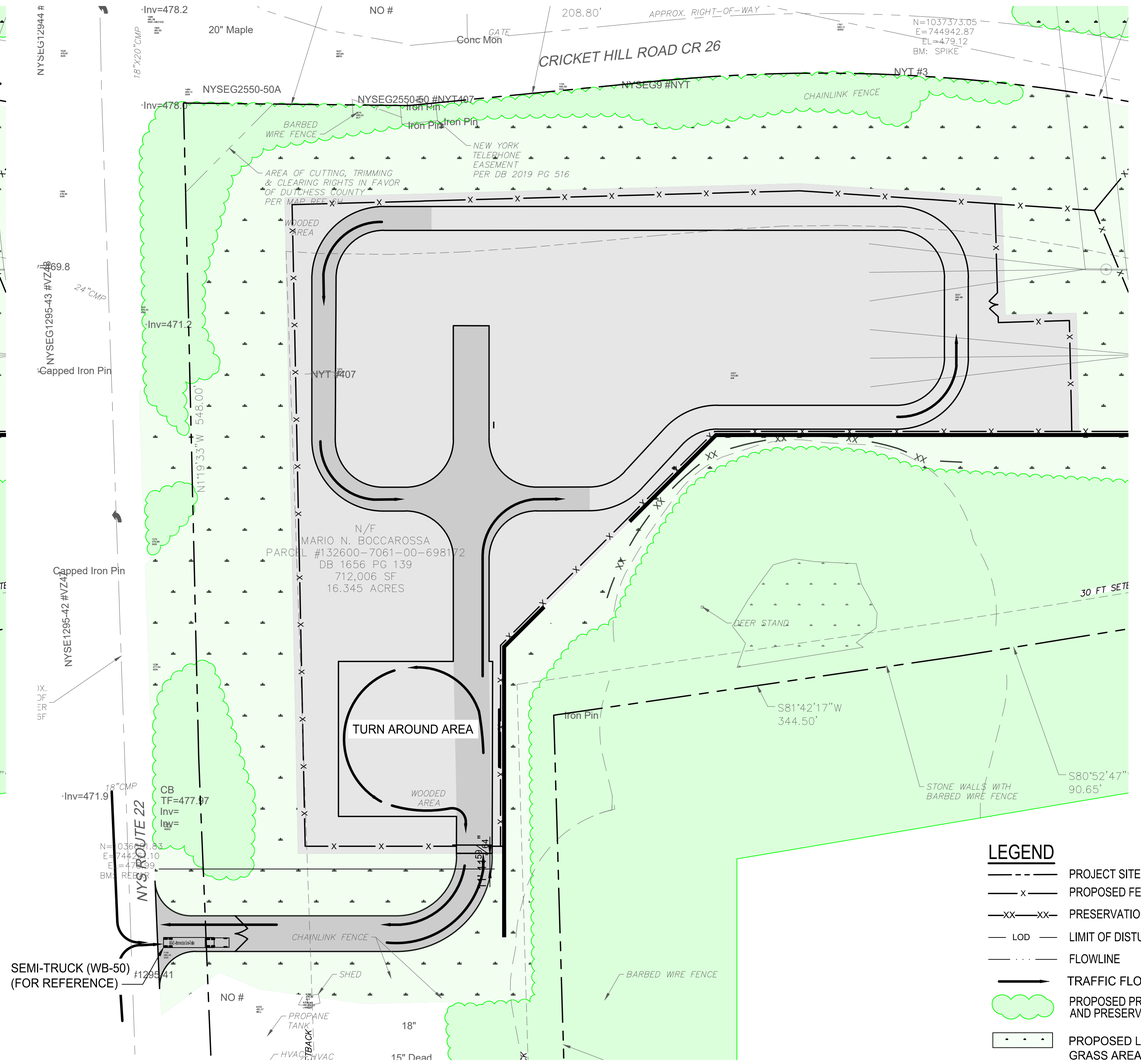

OPERATION

SCALE: 1" = 60'

0 30 60 120 180 FEET

1" = 60'

LEGEND

- PROJECT SITE
- PROPOSED FENCE
- PRESERVATION FENCE
- LIMIT OF DISTURBANCE
- FLOWLINE
- TRAFFIC FLOWLINE
- PROPOSED PRESERVATION LINE AND PRESERVED WOODED AREA
- PROPOSED LANDSCAPE AND GRASS AREAS
- CULVERT
- SUBSTATION AREA SECTION
- ACCESS ROAD SECTION
- RIPRAP
- EXISTING USACE WETLANDS
- EXISTING NYSDEC WETLANDS
- 100-FT WETLAND BUFFER

STATE OF NEW YORK
WILLIAM H. ROMINES, JR
104002
LICENSED PROFESSIONAL ENGINEER

WILLIAM H. ROMINES, JR PE # 104002

PROJECT LOCATION:
2238 ROUTE 22
DOVER, NY 12594

DVB-C1-103.DWG

THIS DRAWING WAS PREPARED BY POWER ENGINEERS, INC. FOR A SPECIFIC PROJECT, TAKING INTO CONSIDERATION THE SPECIFIC AND UNIQUE REQUIREMENTS OF THE PROJECT. REUSE OF THIS DRAWING OR ANY INFORMATION CONTAINED IN THIS DRAWING FOR ANY PURPOSE IS PROHIBITED UNLESS WRITTEN PERMISSION FROM BOTH POWER AND POWER'S CLIENT IS GRANTED.

New York Transco

REV	REVISIONS	DATE	DRN	DSGN	CKD	APPD
C	TOWN OF DOVER PLANNING BOARD SUBMITTAL	08-31-22	BRG	APG	BHR	BHR
B	TOWN OF DOVER PLANNING BOARD SUBMITTAL	04-26-22	BRG	~~BRG~~	BHR	BHR
A	TOWN OF DOVER PLANNING BOARD SUBMITTAL	09-14-21	BRG	BHR	BHR	BHR

REFERENCE DRAWINGS

DSGN	BHR	08-03-21
DRN	BRG	08-03-21
CKD	BHR	08-12-22

SCALE: AS NOTED

FOR 24x36 DWG ONLY

POWER ENGINEERS

NY TRANSCO

DOVER STATION

TRAFFIC FLOW PLAN

JOB NUMBER 169978

REV C

DRAWING NUMBER DVB-C1-103